


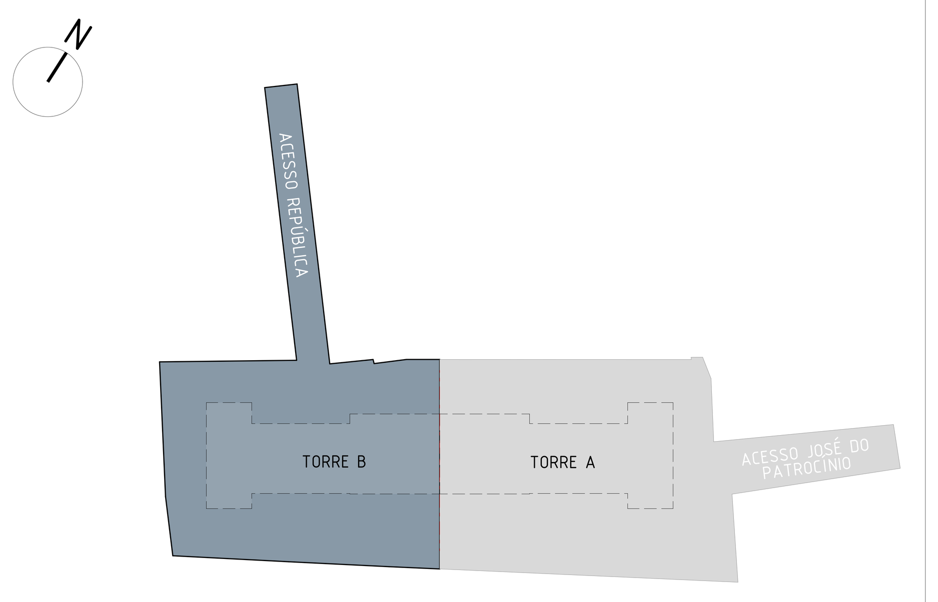

PBP_2º PAVIMENTO
ESCALA 1:75

ACÚSTICA:	INCÊNDIO:
AR CONDICIONADO:	INTERIORES: 7420-EX-INT-BIM-0001-GE-R02
COMUNICAÇÃO VISUAL:	MODULAÇÃO: 7420-EX-MOD-BIM-1000-GE-R05
ELÉTRICA:	PAISAGISMO: 7420-EX-PAI-BIM-0000-GE-R02
ESCADA PRESSURIZADA:	PISCINA:
ESTRUTURAL: 7420-EX-EST-BIM-0000-GER-R00	SEGURANÇA:
GÁS:	SONDAGEM:
HIDRÁULICO:	TOPOGRÁFICO:

ARQUIVOS DE REFERÊNCIA

REV.	DATA	RESPONSÁVEL	DISCRIMINAÇÃO
R06	18/01/2023	ARQ. RAQUEL | ARQ. WALQUIRIA	REVISÕES MELNICK: ATUALIZAÇÃO ACABAMENTO CAPEAMENTOS E RUFOS; INSERÇÃO ESQUIADRIAS PM12 E PM13 15P.
R05	01/12/2022	RAQUEL	ATUALIZAÇÃO CONFORME AJUSTES DETALHAMENTOS E REVISÕES MELNICK.
R04	31/10/2022	RAQUEL	AJUSTES DETALHAMENTOS CONDOMINIAIS, AJUSTE POSICIONAMENTO ESQUADRIA PULMÃO JP
R03	26/09/2022	RAQUEL	REVISÃO DE APONTAMENTOS CONSTRUFLOW TE; AJUSTE ESQUADRIA PULMÕES, SALA GERADOR E HALL CV 2P
R02	22/08/2022	RAQUEL	REVISÃO DE APONTAMENTOS CONSTRUFLOW E AJUSTES GRÁFICOS DE DOCUMENTAÇÃO
R01	10/08/2022	RAQUEL	ATUALIZAÇÃO BASE APOLINÁRIO CONFORME PARECER CB. INCLUSÃO MURO FASE 02 NO PLAYGROUND. REVISÃO APONTAMENTOS CONSTRUFLOW. INDICAÇÃO DE PORTAS COM CONTROLE DE ACESSO E PISOS TÁTEIS NAS ESCADAS E PASSEIOS.
R00	17/07/2022	RAQUEL	EMISSÃO INICIAL

STUDIO
RONALDO
REZENDE
Rua Felipe Neri, 01 | Auxiliadora | CEP: 90440-150
Porto Alegre | RS | Brasil
+55 51 3023.8080 | projetos@ronaldorezende.com.br
Associado AsBEA RS | www.ronaldorezende.com.br

MELNICK EVEN AQUARIUS EMPREENDIMENTOS IMOBILIARIOS LTDA
CONSTRUÇÃO

MELNICK EVEN AQUARIUS EMPREENDIMENTOS IMOBILIARIOS LTDA
PROPRIETÁRIO

ARQ. RONALDO G.C REZENDE | CAU A4713-9
ARQ. RAUL TABASNIK REZENDE | CAU A94249-9

JOSÉ DO PATROCÍNIO
ENDEREÇO
RUA JOSÉ DO PATROCÍNIO, 527 | RUA DA REPÚBLICA, 574

DESENHO
ARQ. JOÃO DIAS COELHO | ARQ. RAQUEL FARIA | ARQ. VITÓRIA VILLAS BÔAS | ARQ. LUIZA ARNT ARQ. ADRIANA DALMÁS

REVISÃO

VERSÃO
R06

FASE PROJETO
0001 Executivo_PBP

ESCALA
1:75, 1:500

DATA
18/01/2023

CONTEÚDO
PLANTA BAIXA 2° PAVIMENTO TORRE B

PRANCHA
002B

ARQUIVO DIGITAL
7420-EX-ARQ-BIM-0001-GE-R08

PROCESSO Nº