
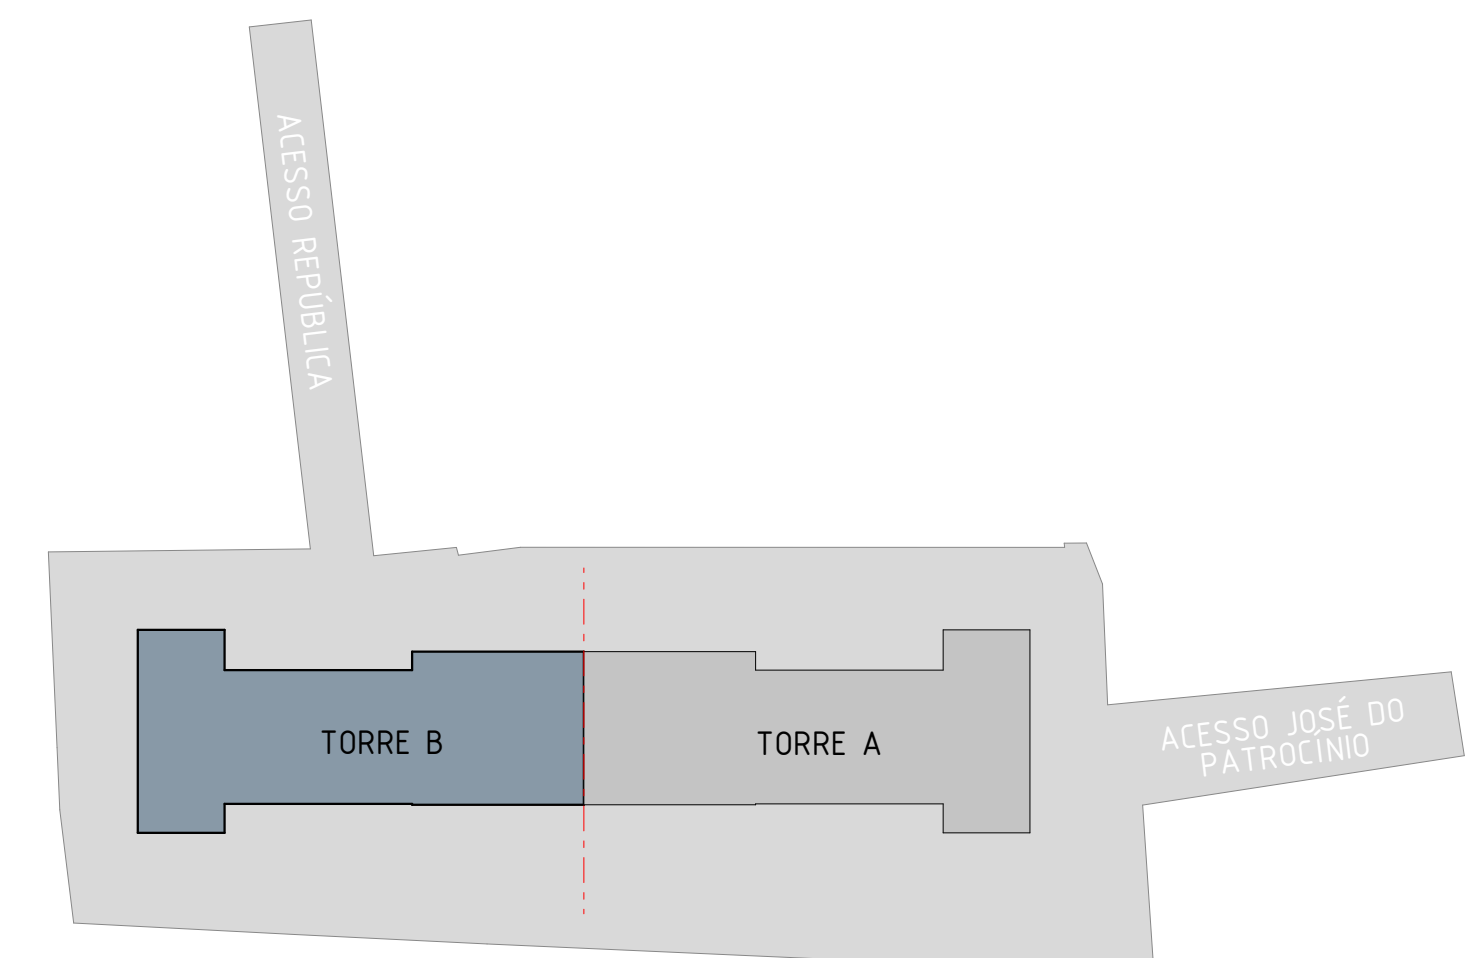
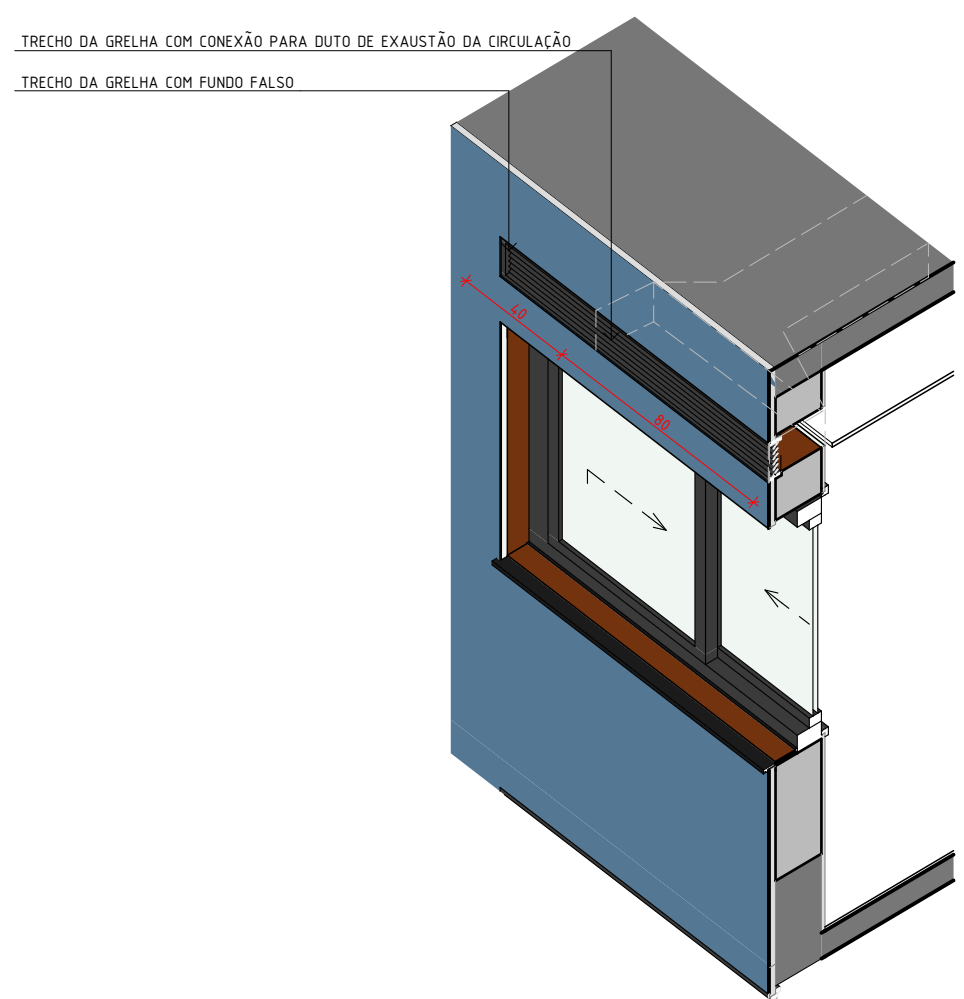
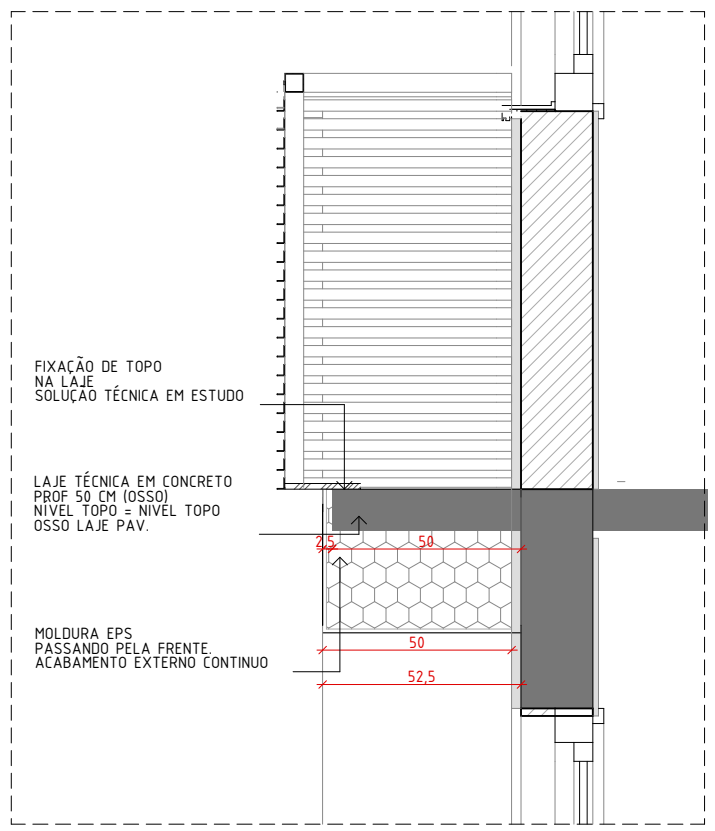
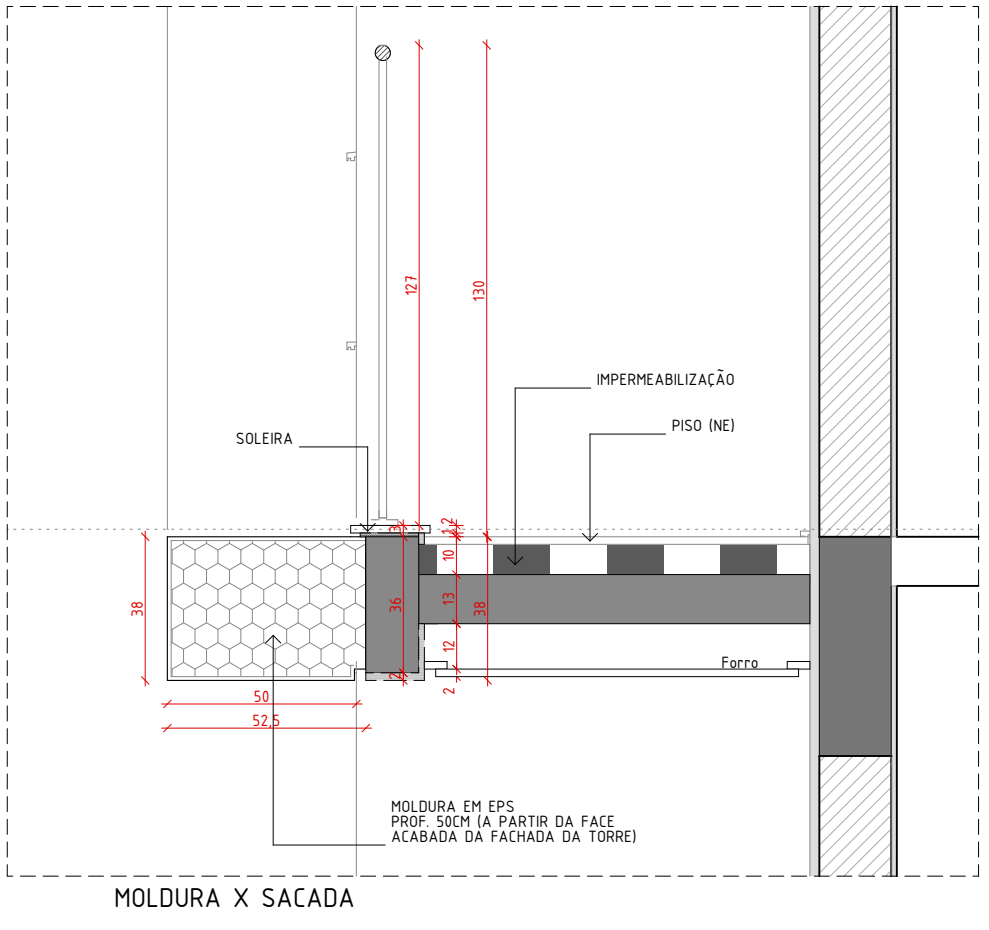
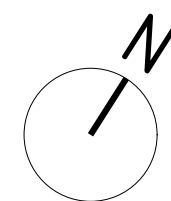


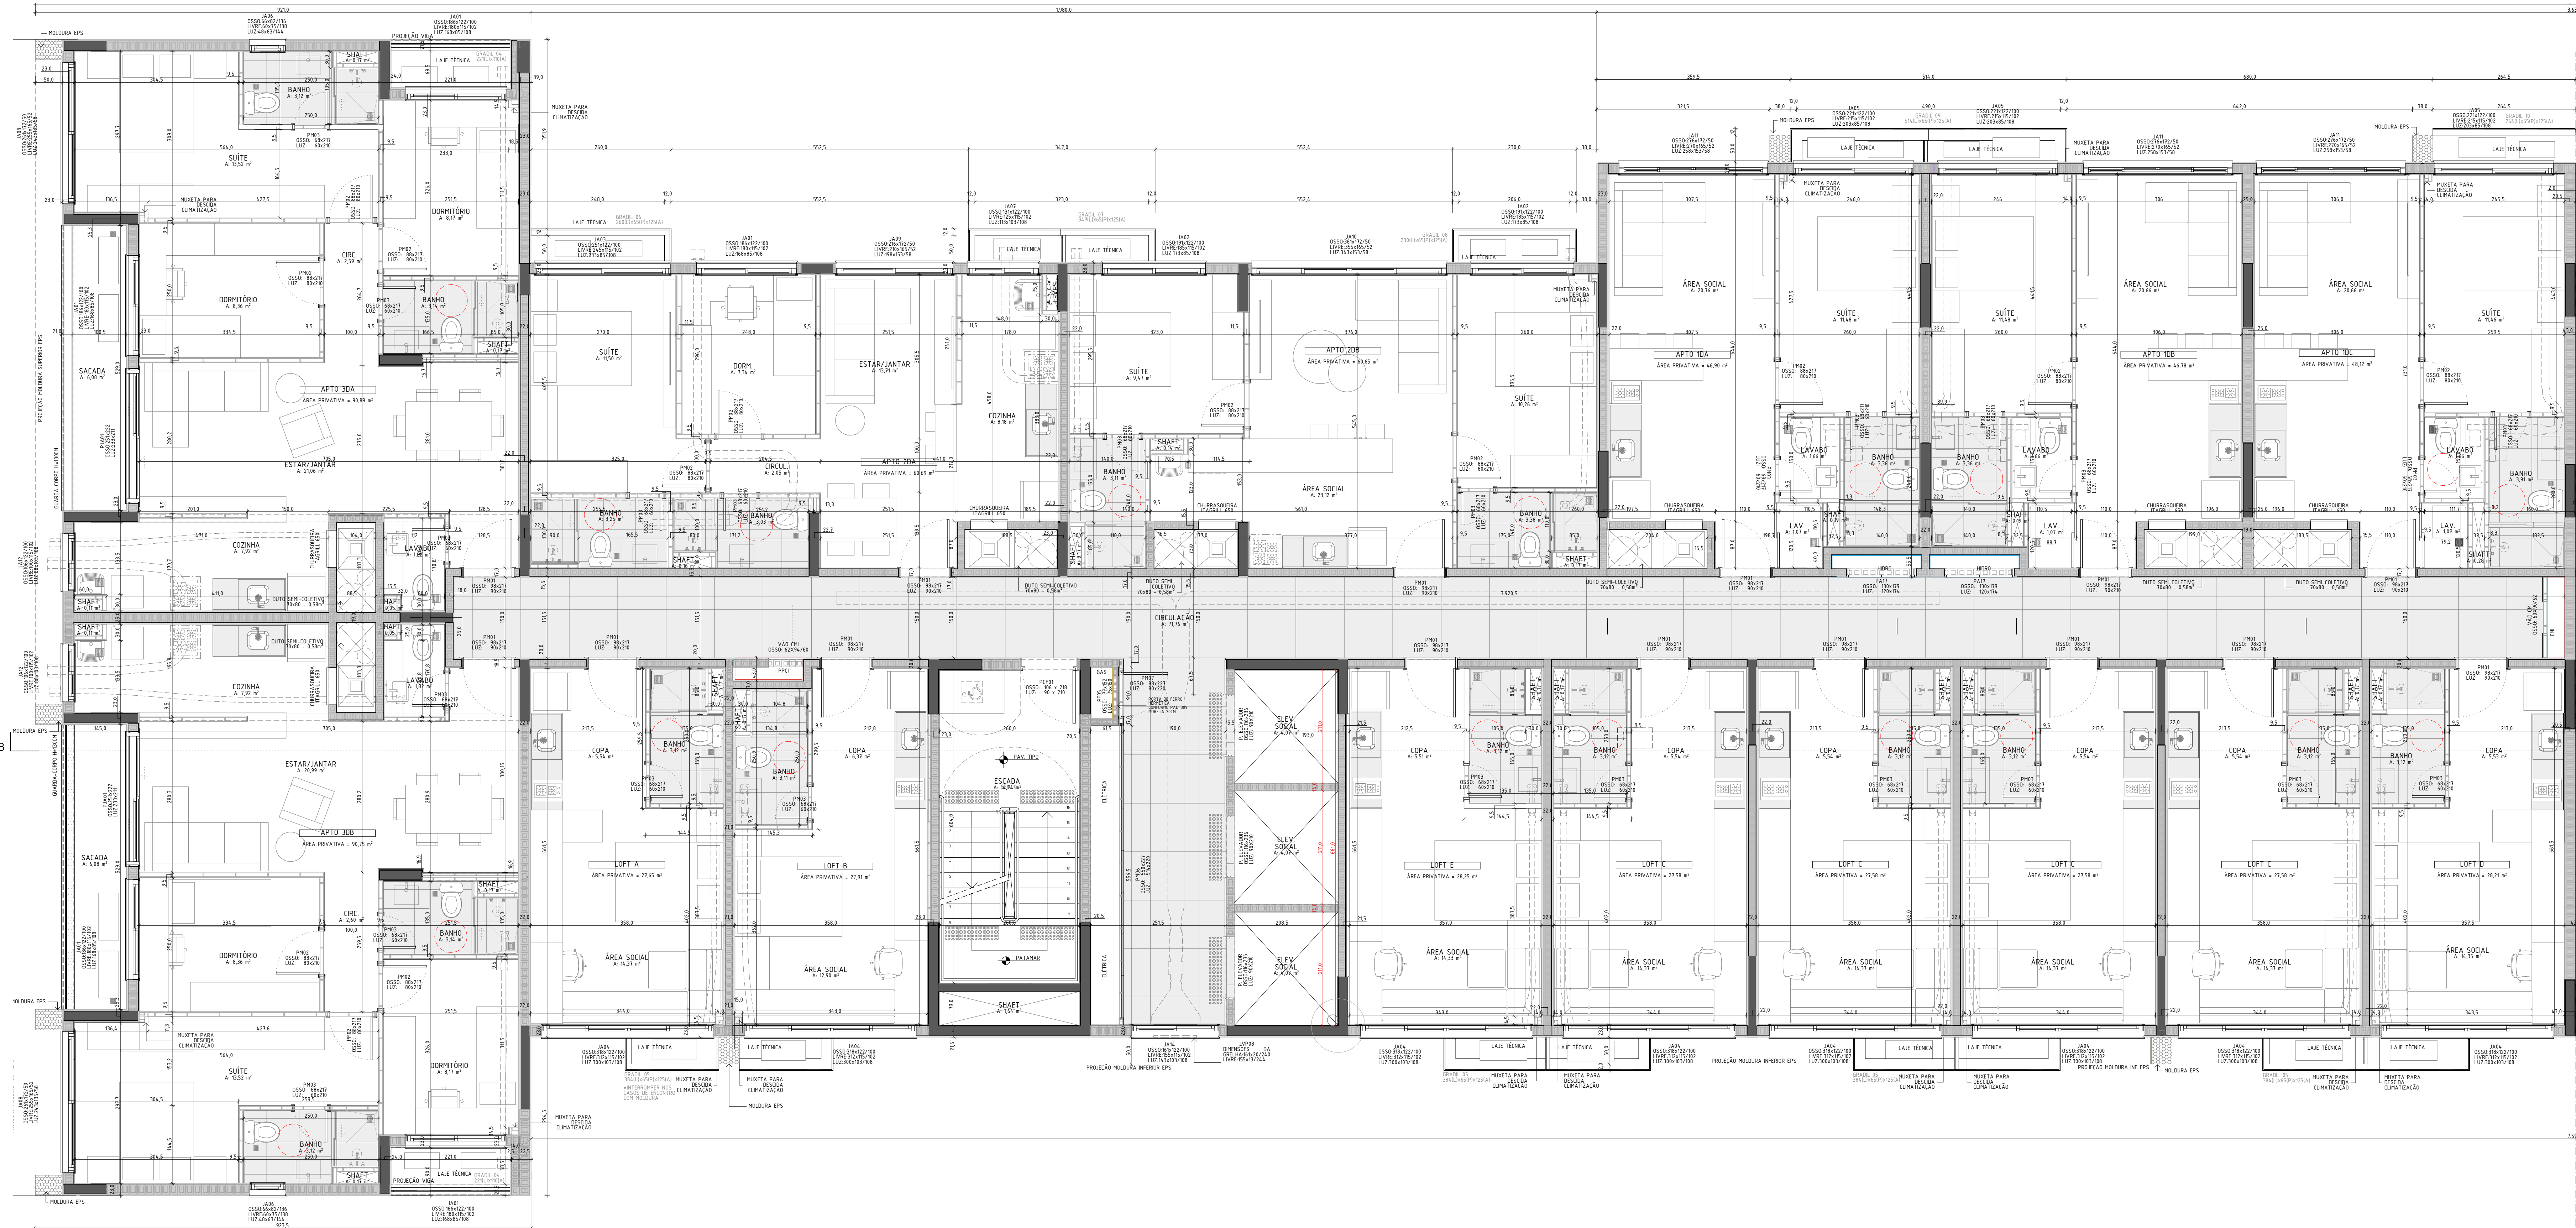

*ESTÃO CONSIDERADOS NAS ÁREAS PRIVATIVAS, PARA ALÉM DAS ÁREAS INTERNAS DE CADA UNIDADE E SUAS SACADAS, OS TRECHOS DAS LAJES TÉCNICAS.			
ACUSTICA		INCÊNDIO	
AB CONDICIONADO		INTERIORES 7420-EX-INT-BM-0001-GE-R02	
COMUNICAÇÃO VISUAL		MODULAÇÃO 7420-EX-MOD-BM-0001-GE-R05	
ELÉTRICA		PAISAGISMO 7420-EX-PAI-BM-0000-GE-R02	
ESCALA PRESSURIZADA		SEGURANÇA	
ESTRUTURAL 7420-EX-EST-BM-0000-GER-R03		LUMINOTÉCNICO 7420-EX-LUM-BM-0000-GE-R00	
GÁS		TOPOGRÁFICO	
HIDRÁULICO		ARQUIVOS DE REFERÊNCIA	
R05		10/05/2023	
ARQ. RAQUEL		ARQ. WALQUIRIA	
R05		14/04/2023	
ARQ. RAQUEL		ARQ. WALQUIRIA	
R04		01/12/2022	
RAQUEL		ATUALIZAÇÃO CONFORME AJUSTES DETALHAMENTOS E REVISÕES MELNICK	
R03		08/09/2022	
RAQUEL		REVISÃO DE APONTAMENTOS CONSTRUTIVO INCLUSÃO PORTA HEMÉTICA GÁS (PFGS)	
R01		22/08/2022	
RAQUEL		REVISÃO DE APONTAMENTOS CONSTRUTIVO E AJUSTES GRÁFICOS DE DOCUMENTAÇÃO	
R00		11/07/2022	
RAQUEL		EMISSÃO INICIAL	
REV.		DATA	
RESPONSÁVEL		DISCRIMINAÇÃO	

PLANTA BAIXA PAV. TIPO. 3PAV AO 13PAV.
ESCALA 1:50
OBS: MOLDURAS REFERENTES AO 4PAV.

STUDIO RONALDO REZENDE

Rua Felipe Ney, 61 | Autódromo | CEP: 50445-100
Porto Alegre, RS | Brasil
+55 51 3833 8888 | projeto@studioresende.com.br
Associação ARQ&B | www.studioresende.com.br

HELNICK EVEN AQUARIUS EMPREENDIMENTOS IMOBILIÁRIOS LTDA

CONSTRUTORA

HELNICK EVEN AQUARIUS EMPREENDIMENTOS IMOBILIÁRIOS LTDA

PROPRIETÁRIO

ARQ. RONALDO G. REZENDE | CAU 41378-9

ARQ. RAUL TABAKIAN REZENDE | CAU 41424-5

JOSÉ DO PATROCÍNIO

ENDEREÇO

RUA JOSÉ DO PATROCÍNIO, 527 | RUA DA REPÚBLICA, 574

DESENHO

ARQ. ADÃO DAS COELHO | ARQ. RAQUEL FARIAS | ARQ. VITÓRIA VILLAS BÔAS | ARQ. LUIZA ABNT | ARQ. ADRIANA DALMAS

FASE PROJETO

Executivo_PBP

ESCALA

1:50, 1:75, 1:20, 1:25, 1:500

DATA

10/05/2023

PRONCHIA

PROCESSO Nº

003B