A
B
LAJE TÉCNICA
MOLDURA EPS
PROJEÇÃO MOLDURA EPS
MUXETA PARA DESCIDA CLIMATIZAÇÃO
SUÍTE A: 11,46 m²
ÁREA SOCIAL A: 20,66 m²
APTO 1DC
ÁREA PRIVATIVA = 48,12 m²
APTO 1DB
ÁREA PRIVATIVA = 46,78 m²
APTO 1DA
ÁREA PRIVATIVA = 46,90 m²
SUÍTE A: 11,47 m²
SUÍTE A: 11,48 m²
LAVABO A: 1,65 m²
BANHO A: 3,92 m²
LAV. A: 1,08 m²
BANHO A: 3,36 m²
LAVABO A: 1,63 m²
LAV. A: 1,07 m²
CHURRASQUEIRA ITAGRILL 650
HIDRO
PA17 OSSO: 130x179 LUZ: 120x174
DUTO SEMI-COLETIVO 70x80 - 0,58m²
PM01 OSSO: 98x217 LUZ: 90x210
PM02 OSSO: 88x217 LUZ: 80x210
PM03 OSSO: 68x217 LUZ: 60x210
CMI
VÃO CMI OSSO: 60X90/62
APTO 2DB
ÁREA PRIVATIVA = 60,65 m²
SUÍTE A: 10,20 m²
ÁREA SOCIAL A: 23,11 m²
SUÍTE A: 9,51 m²
BANHO A: 3,11 m²
SHAFT A: 0,14 m²
COZINHA A: 8,18 m²
APTO 2DA
ÁREA PRIVATIVA = 60,69 m²
ESTAR/JANTAR A: 13,71 m²
DORM. A: 7,34 m²
SUÍTE A: 11,50 m²
CIRCUL. A: 2,05 m²
BANHO A: 3,03 m²
BANHO A: 3,24 m²
S-68
CIRCULAÇÃO A: 71,76 m²
APTO 3DA
ÁREA PRIVATIVA = 90,89 m²
DORMITÓRIO A: 8,17 m²
SUÍTE A: 13,57 m²
BANHO A: 3,12 m²
BANHO A: 3,14 m²
CIRC. A: 2,59 m²
DORMITÓRIO A: 8,36 m²
ESTAR/JANTAR A: 21,02 m²
SACADA A: 6,08 m²
GUARDA-CORPO H=130CM
LAVABO A: 1,82 m²
COZINHA A: 7,92 m²
PROJEÇÃO MOLDURA EPS
PROJEÇÃO VIGA
LOFT D
ÁREA PRIVATIVA = 28,21 m²
LOFT C
ÁREA PRIVATIVA = 27,58 m²
LOFT E
ÁREA PRIVATIVA = 28,25 m²
COPA A: 5,53 m²
COPA A: 5,54 m²
COPA A: 5,51 m²
BANHO A: 3,12 m²
ÁREA SOCIAL A: 14,35 m²
ÁREA SOCIAL A: 14,37 m²
ÁREA SOCIAL A: 14,33 m²
ELEV. SOCIAL A: 4,07 m²
P. ELEVADOR OSSO:116x236 LUZ: 90X210
PM07 OSSO: 88x227 LUZ: 80x220
PORTA DE FERRO HERMÉTICA CONFORME PAD-309 MURETA 20CM
GÁS
PF05 OSSO: 77x152 LUZ: 75x150
ELÉTRICA
ESCADA A: 14,70 m²
VAI DO 3º PAVIMENTO
VÃO CMI OSSO: 65X94/60
PPCI
LOFT B
ÁREA PRIVATIVA = 27,91 m²
COPA A: 6,36 m²
BANHO A: 3,11 m²
ÁREA SOCIAL A: 12,90 m²
LOFT A
ÁREA PRIVATIVA = 27,65 m²
ÁREA SOCIAL A: 14,37 m²
APTO 3DB
ÁREA PRIVATIVA = 90,74 m²
ESTAR/JANTAR A: 21,00 m²
CIRC. A: 2,60 m²
DORMITÓRIO A: 8,36 m²
JA04 OSSO:318x122/100 LIVRE:312x115/102 LUZ:300x103/108
JA14 OSSO:161x122/100 LIVRE:155x115/102 LUZ:143x103/108
JA01 OSSO:186x122/100 LIVRE:180x115/102 LUZ:168x85/108
JA06 OSSO:66x82/136 LIVRE:60x75/138 LUZ:48x63/144

PLANTA BAIXA 14º PAVIMENTO
ESCALA 1:50

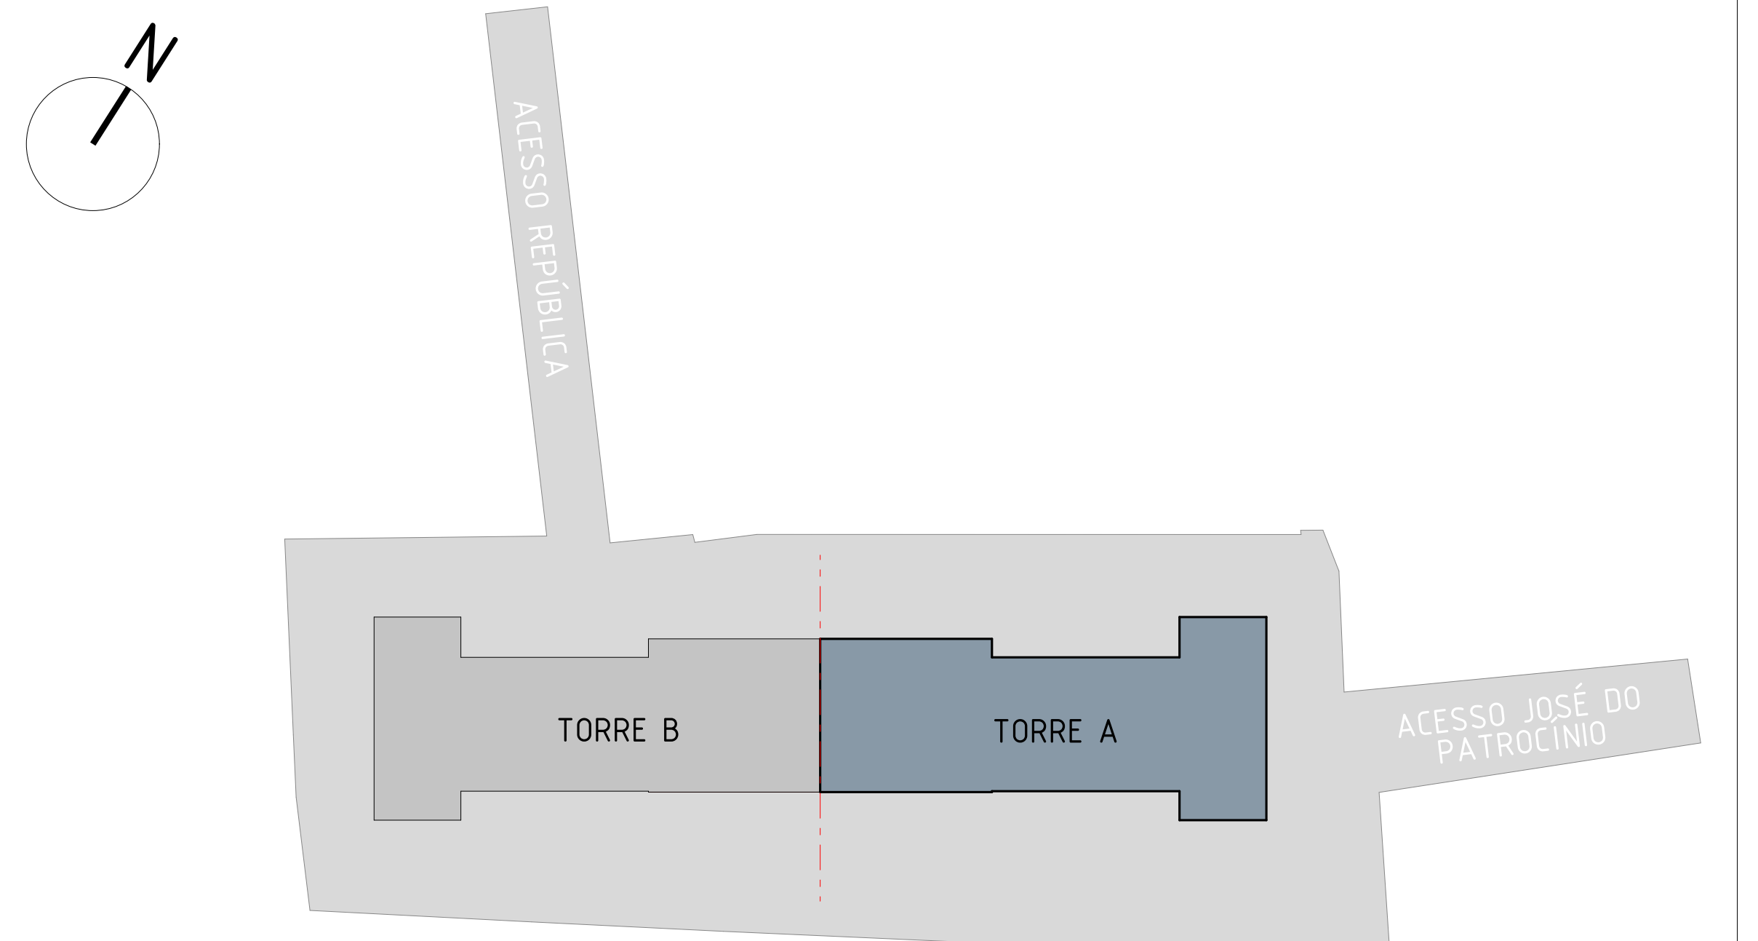
N
ACESSO REPÚBLICA
TORRE B
TORRE A
ACESSO JOSÉ DO PATROCÍNIO

*ESTÃO CONSIDERADOS NAS ÁREAS PRIVATIVAS, PARA ALÉM DAS ÁREAS INTERNAS DE CADA UNIDADE E SUAS SACADAS, OS TRECHOS DAS LAJES TÉCNICAS.

ACÚSTICA:	INCÊNDIO:
AR CONDICIONADO:	INTERIORES: 7420-EX-INT-BIM-0001-GE-R02
COMUNICAÇÃO VISUAL:	MODULAÇÃO: 7420-EX-MOD-BIM-1000-GE-R05
ELÉTRICA:	PAISAGISMO: 7420-EX-PAI-BIM-0000-GE-R02
ESCADA PRESSURIZADA:	PISCINA:
ESTRUTURAL: 7420-EX-EST-BIM-0000-GER-R00	SEGURANÇA:
GÁS:	IMPERMEABILIZAÇÃO:
HIDRÁULICO:	TOPOGRÁFICO:

ARQUIVOS DE REFERÊNCIA

REV.	DATA	RESPONSÁVEL	DISCRIMINAÇÃO
R06	10/05/2023	ARQ. RAQUEL | ARQ. WALQUIRIA	AUMENTO 4cm ALTURA PA17
R05	14/04/2023	ARQ. RAQUEL | ARQ. WALQUIRIA	AJUSTE PORTA SHAFT HIDRO NA CIRCULAÇÃO DO TIPO (PA17)
R04	01/12/2022	RAQUEL	ATUALIZAÇÃO CONFORME AJUSTES DETALHAMENTOS E REVISÕES MELNICK.
R03	08/09/2022	RAQUEL	AJUSTE SHAFTS LIXO E GUARITA JP, REVISÕES PENAS E AJUSTES GRAFICAÇÃO
R02	30/08/2022	RAQUEL	REVISÃO DE APONTAMENTOS CONSTRUFLOW. INCLUSÃO PORTA HERMÉTICA GÁS (PF05).
R01	22/08/2022	RAQUEL	REVISÃO DE APONTAMENTOS CONSTRUFLOW E AJUSTES GRÁFICOS DE DOCUMENTAÇÃO
R00	17/07/2022	RAQUEL	EMISSÃO INICIAL

**STUDIO
RONALDO
REZENDE**

Rua Felipe Neri, 01 | Auxiliadora | CEP: 90440-150
Porto Alegre | RS | Brasil
+55 51 3023.8080 | projetos@ronaldorezende.com.br
Associado AsBEA RS | www.ronaldorezende.com.br

MELNICK EVEN AQUARIUS EMPREENDIMENTOS IMOBILIARIOS LTDA
CONSTRUÇÃO

MELNICK EVEN AQUARIUS EMPREENDIMENTOS IMOBILIARIOS LTDA
PROPRIETÁRIO

ARQ. RONALDO G.C REZENDE | CAU A4713-9
ARQ. RAUL TABASNIK REZENDE | CAU A94249-9

JOSÉ DO PATROCÍNIO
ENDEREÇO
RUA JOSÉ DO PATROCÍNIO, 527 | RUA DA REPÚBLICA, 574

DESENHO
ARQ. JOÃO DIAS COELHO | ARQ. RAQUEL FARIA | ARQ. VITÓRIA VILLAS BÔAS | ARQ. LUIZA ARNT
REVISÃO
ARQ. ADRIANA DALMÁS
VERSÃO
R06

FASE PROJETO
Executivo_PBP
ESCALA
1:50, 1:75, 1:500
DATA
10/05/2023
CONTEÚDO
PLANTA BAIXA 14° PAVIMENTO - TORRE A
PRANCHA
004A
ARQUIVO DIGITAL
7420-EX-ARQ-BIM-0001-GE-R08
PROCESSO Nº