
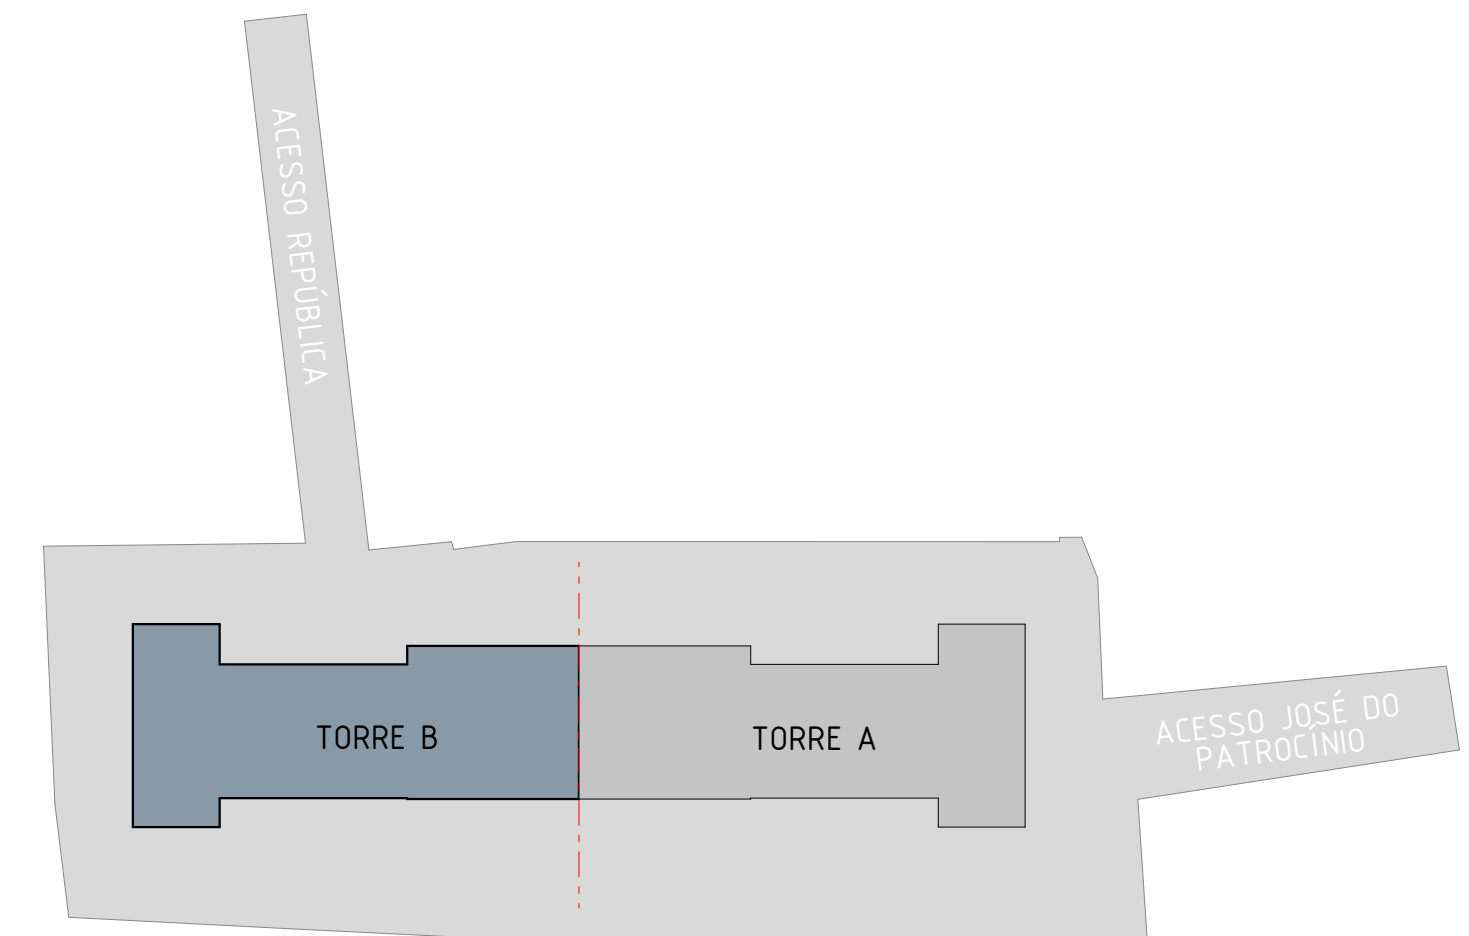
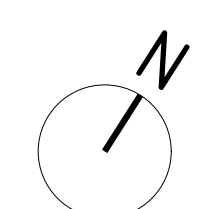


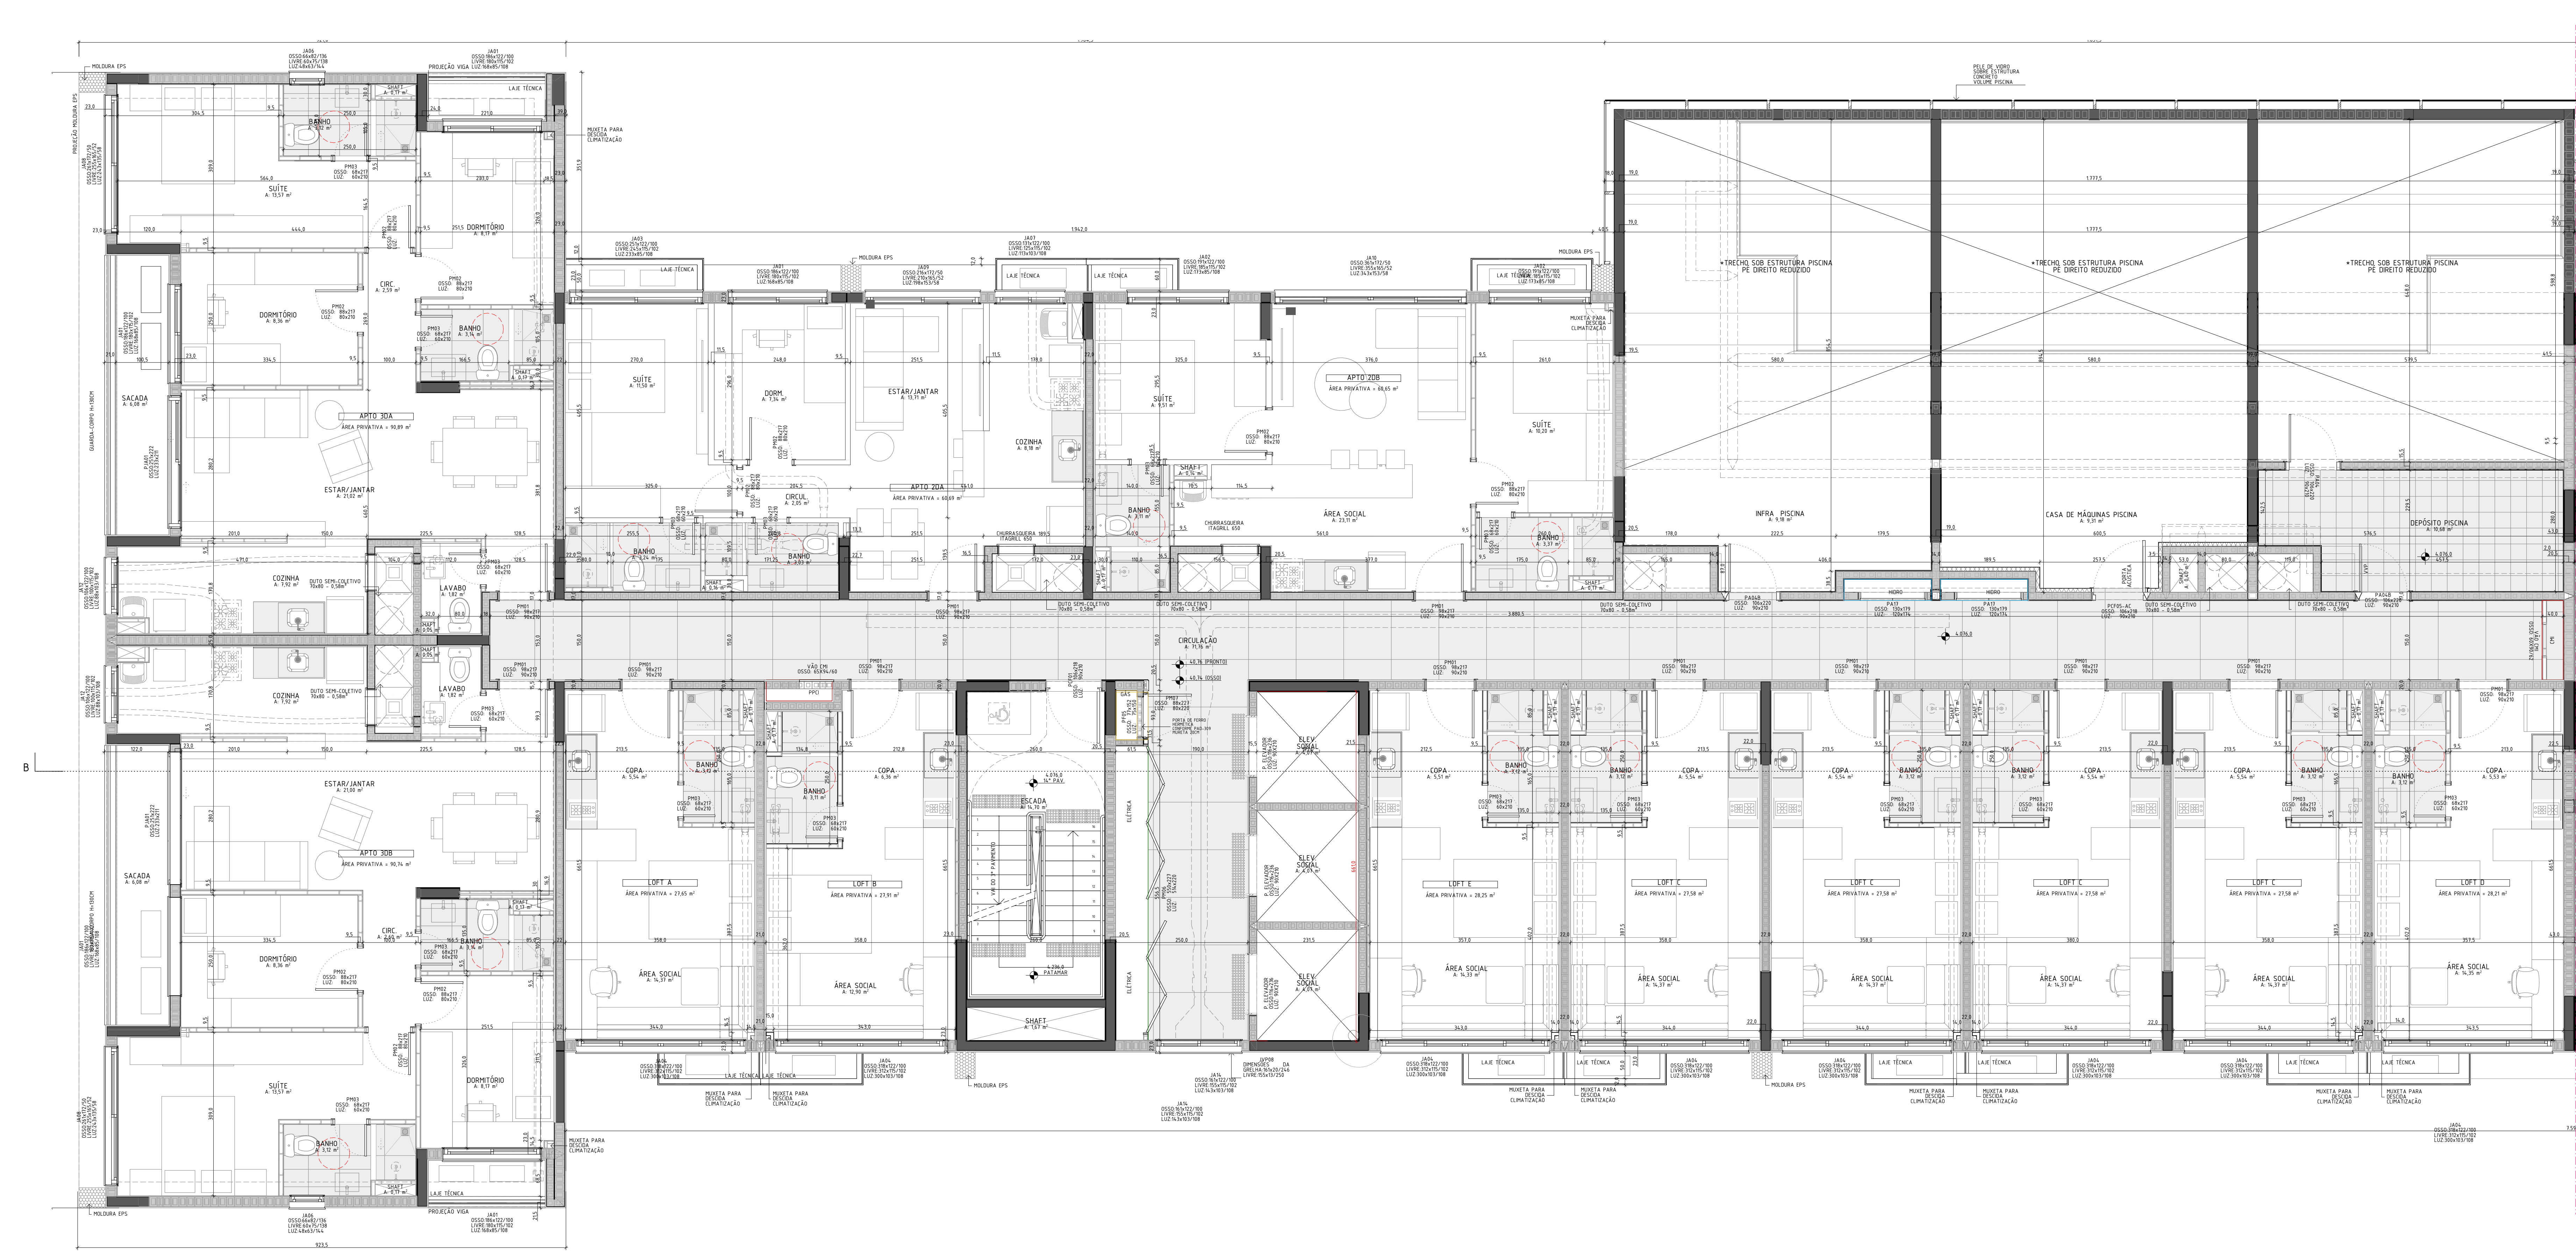

+ESTÃO CONSIDERADOS, NAS ÁREAS PRIVATIVAS, PARA ALÉM DAS ÁREAS INTERNAS DE CADA UNIDADE E SUAS SACADAS, OS TRECHOS DAS LAJES TÉCNICAS.

ACÚSTICA				INCÊNDIO			
AR CONDICIONADO				INTERIORES: 7420-EX-INT-BM-0001-GE-R02			
COMUNICAÇÃO VISUAL				MODULAÇÃO: 7420-EX-MOD-BM-0001-GE-R05			
ELÉTRICA				PASSAGIEMO: 7420-EX-PAI-BM-0001-GE-R02			
ESTRUTURAL: 7420-EX-EST-BM-0001-GER-R00				PISCINA			
GÁS				SEGURANÇA			
HIDRÁULICO				IMPERMEABILIZAÇÃO			
				TOPOGRÁFICO			
				ARQUIVOS DE REFERÊNCIA			
R06	10/05/2023	ARG. RAQUEL	ARG. WALQUIRIA	AUMENTO 4cm ALTURA PA17			
R05	14/04/2023	ARG. RAQUEL	ARG. WALQUIRIA	AJUSTE PORTA SHAFT HDRO NA CIRCULAÇÃO DO TIPO (PA17)			
R04	01/02/2022	RAQUEL		ATUALIZAÇÃO CONFORME AJUSTES DETALHAMENTOS E REVISÕES MELNICK			
R03	08/09/2022	RAQUEL		AJUSTE SHAFTS LIXO E GUARITA JP, REVISÕES PENAS E AJUSTES GRAFICAÇÃO			
R02	30/08/2022	RAQUEL		REVISÃO DE APONTAMENTOS CONSTRUFLOW E AJUSTES PORTA HERMÉTICA GAS (PP05)			
R01	22/08/2022	RAQUEL		REVISÃO DE APONTAMENTOS CONSTRUFLOW E AJUSTES GRÁFICOS DE DOCUMENTAÇÃO			
R00	17/07/2022	RAQUEL		EMIÇÃO INICIAL			
REV.	DATA	RESPONSÁVEL		DISCRIMINAÇÃO			

STUDIO RONALDO REZENDE

Rua Félix Neto, 87 | Ascendia | CEP: 98445-500
Porto Alegre | RS | Brasil
+55 51 3023.8000 | projeto@studioresende.com.br
Assinatura: [Assinatura](#) | [www.studioresende.com.br](#)

MELNICK EVEN AQUARIUS EMPREENDIMENTOS IMOBILIÁRIOS LTDA
CONSTRUÇÃO

MELNICK EVEN AQUARIUS EMPREENDIMENTOS IMOBILIÁRIOS LTDA
PROJETADO

ARG. RONALDO G.C. REZENDE | CAU A4713-9
ARG. RAUL TABASKIN REZENDE | CAU A94243-9

PLANTA BAIXA 14º PAVIMENTO
ESCALA 150

JOSÉ DO PATROCÍNIO				R06			
PROJETO				175, 1500, 150			
FÁSE PROJETO				10/05/2023			
Executivo_PBP				PROJETO			
CONTÉUDO				PROCESSO Nº			
ARQUIVO DIGITAL				004B			
7420-EX-ARG-BM-0001-GE-R08							