
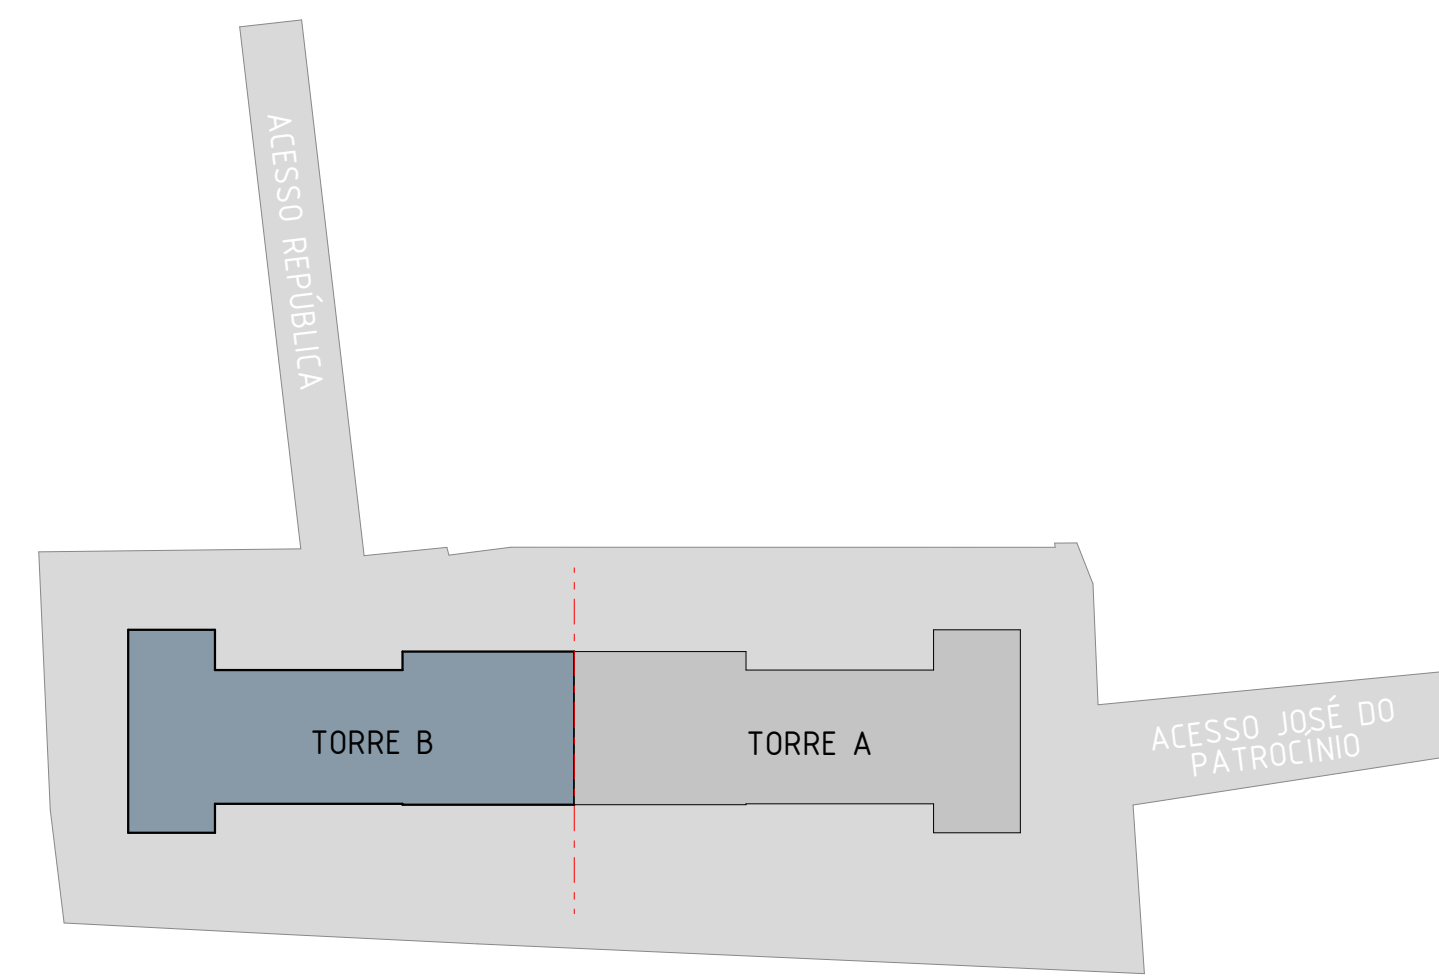


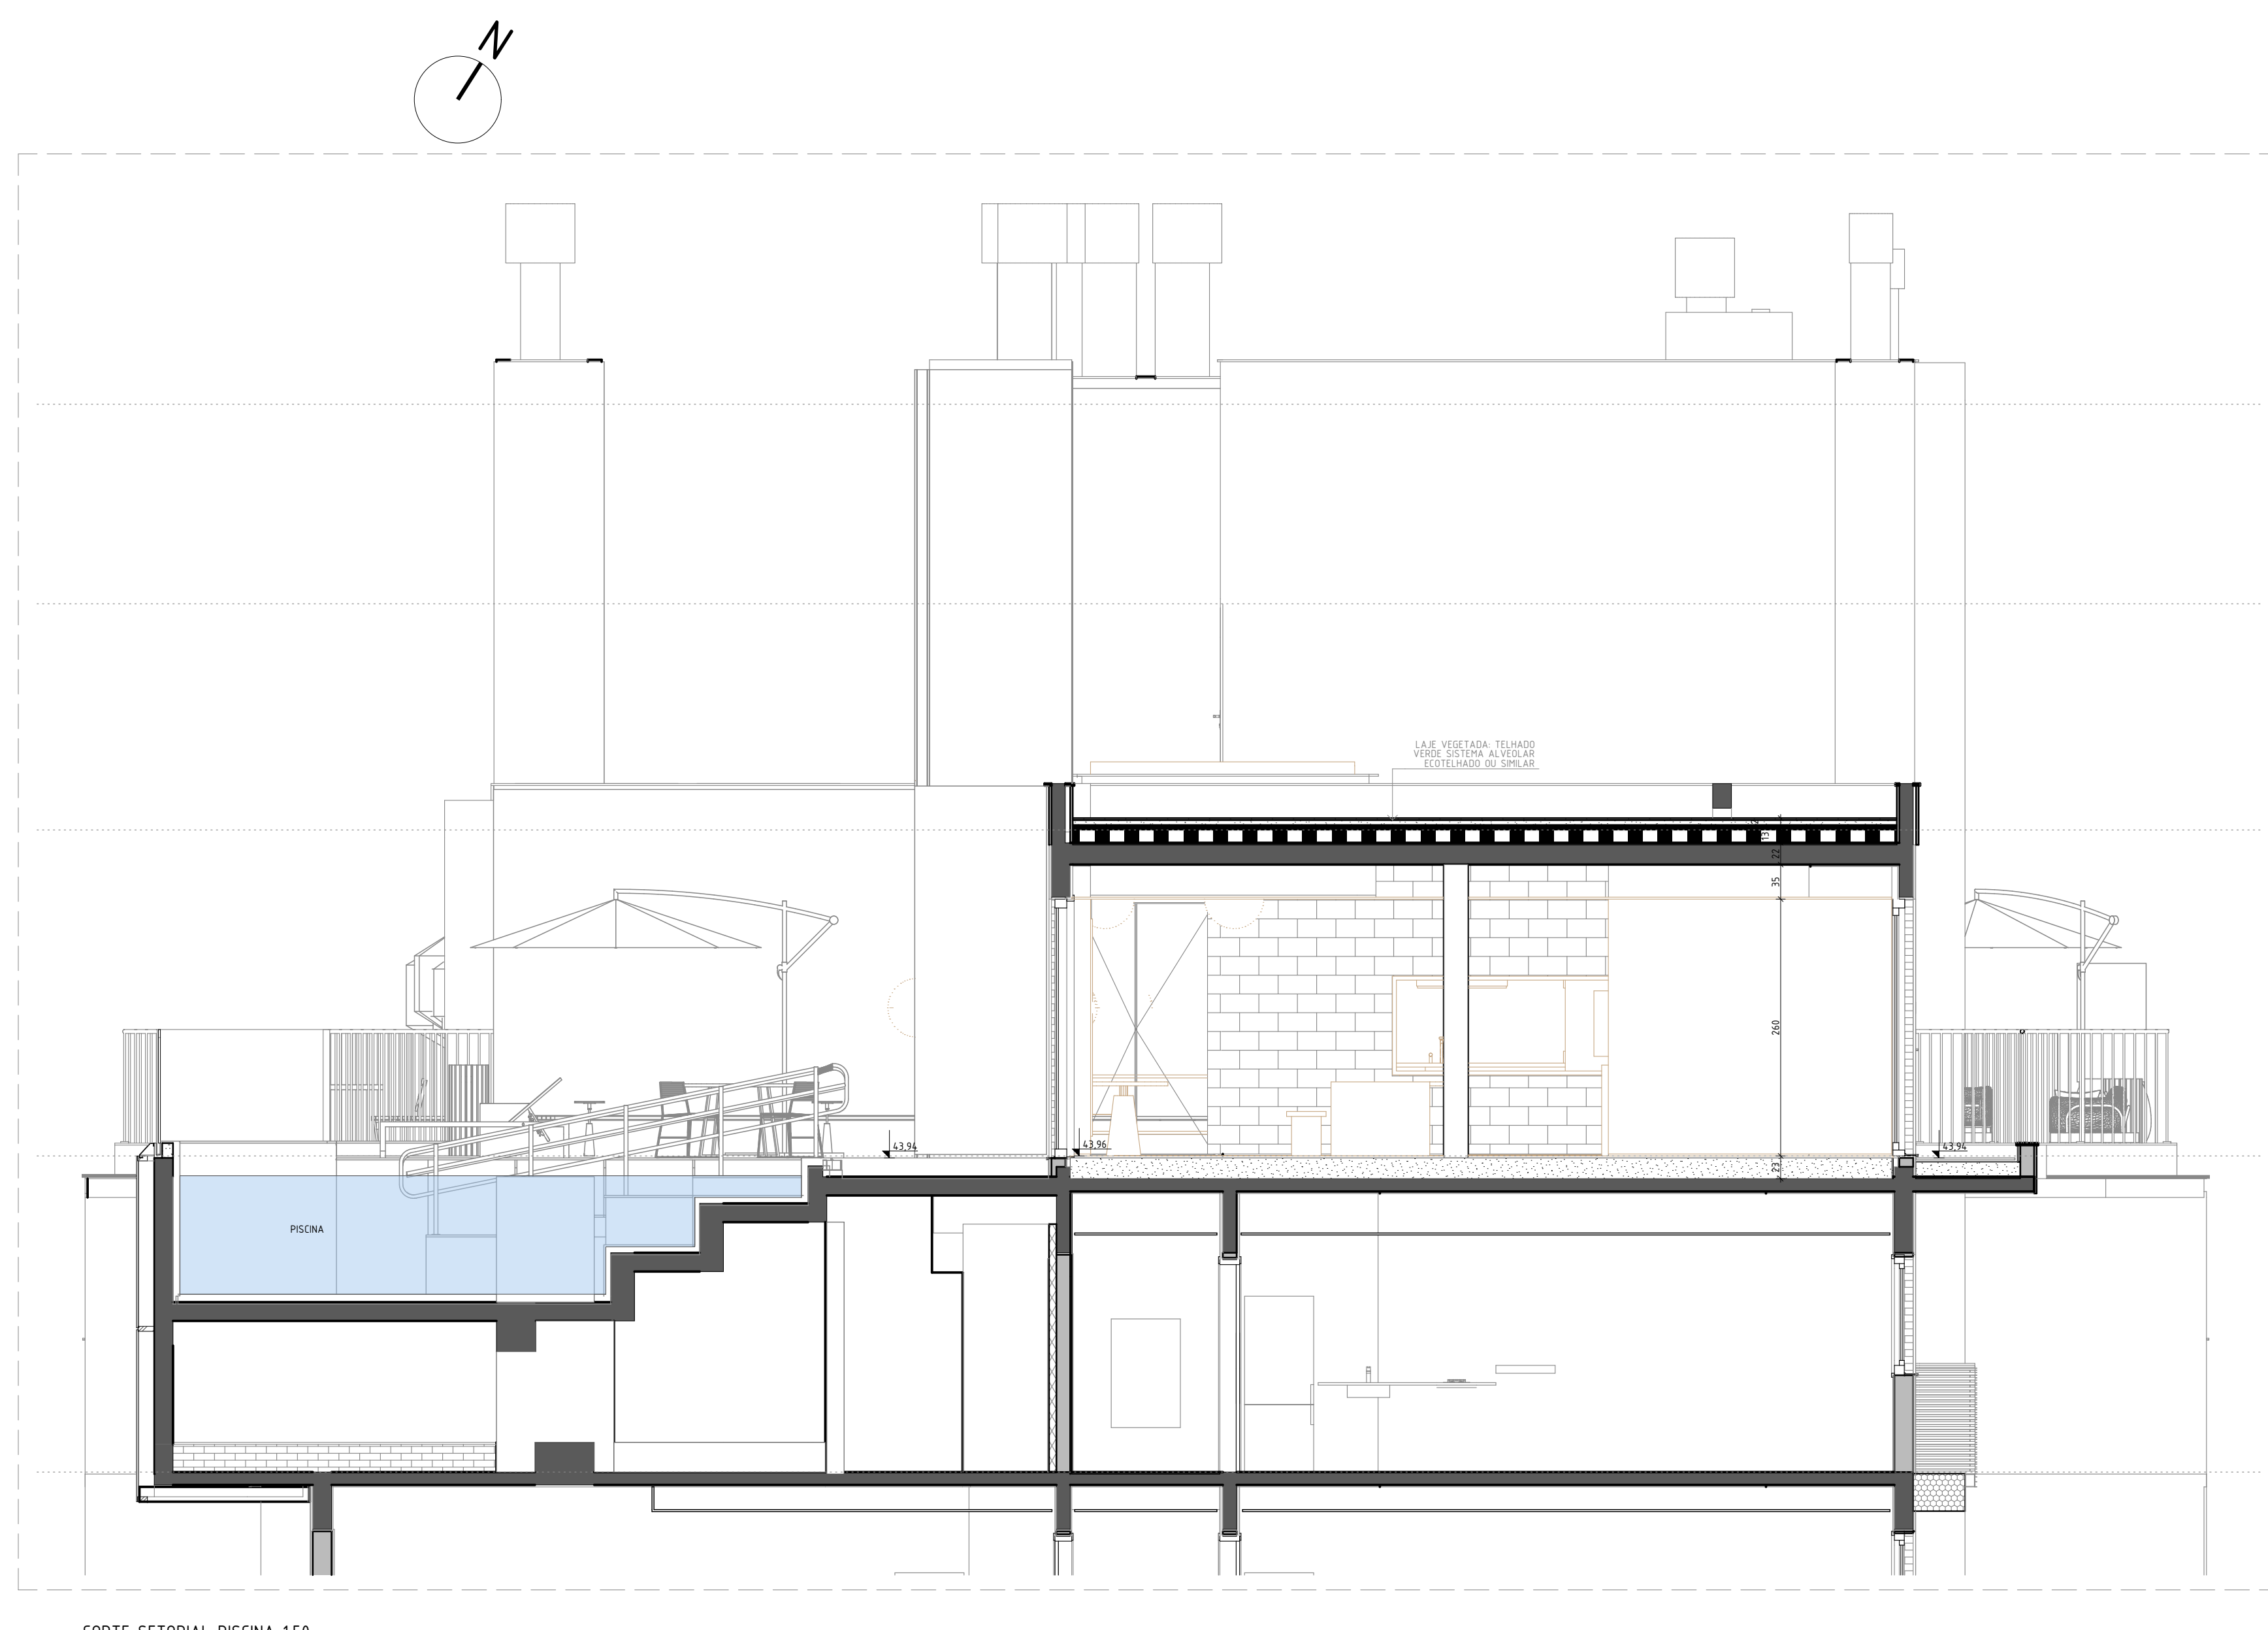

*ESTÃO CONSIDERADOS NAS ÁREAS PRIVATIVAS, PARA ALÉM DAS ÁREAS INTERNAS DE CADA UNIDADE E SUAS SACADAS, OS TRECHOS DAS LAJES TÉCNICAS.

[illegible]

STUDIO RONALDO REZENDE

Rua Arlene Nery, 41 | Jussaraíba | CEP: 04144-200
Barra do Piraí - RJ | Brasil
+55 31 3822 8800 | contato@studio-rezende.com.br
Arquiteto: ARQUITEXA® | www.studio-rezende.com.br

MELNICK: EVEN AGUIARIS EMPREENDIMENTOS IMOBILIÁRIOS LTDA
CONTROLE:

MELNICK: EVEN AGUIARIS EMPREENDIMENTOS IMOBILIÁRIOS LTDA
PROPOSTA Nº:

ARGO, RONALDO C.C. REZENDE | CAU AT-013-1-
ARGO RAUL TABAKSON REZENDE | CAU AN-014-1-1

JOSÉ DO PATROCÍNIO

ENFERMEIRO

RUA JOSÉ DO PATROCÍNIO, 157 | RUA DA REPÚBLICA, 174

GESIMAS

ARGO JOÃO DAS COELHO | ARGO RAQUEL FARRA | ARGO VITÓRIA VELLAS ROAS | ARGO LUÍZA AMINT

REVISED | ARGO ADRIANA DALMÁS

VERSÃO

ESCALA:
150, 175, 150

DATADA
06/07/2021

PRONANCIA

PLANTA BAIXA 15º PAVIMENTO TORRE B

ARGUMENTO DATA: 7/2/21 E-ARGO-BH-001-GE-008

005B